

A

B

C

D

E

F


DRG NO.:

TITLE:

CHANGES VIA CAD ONLY

INCOMING
SUPPLY
50 Hz.

12345678

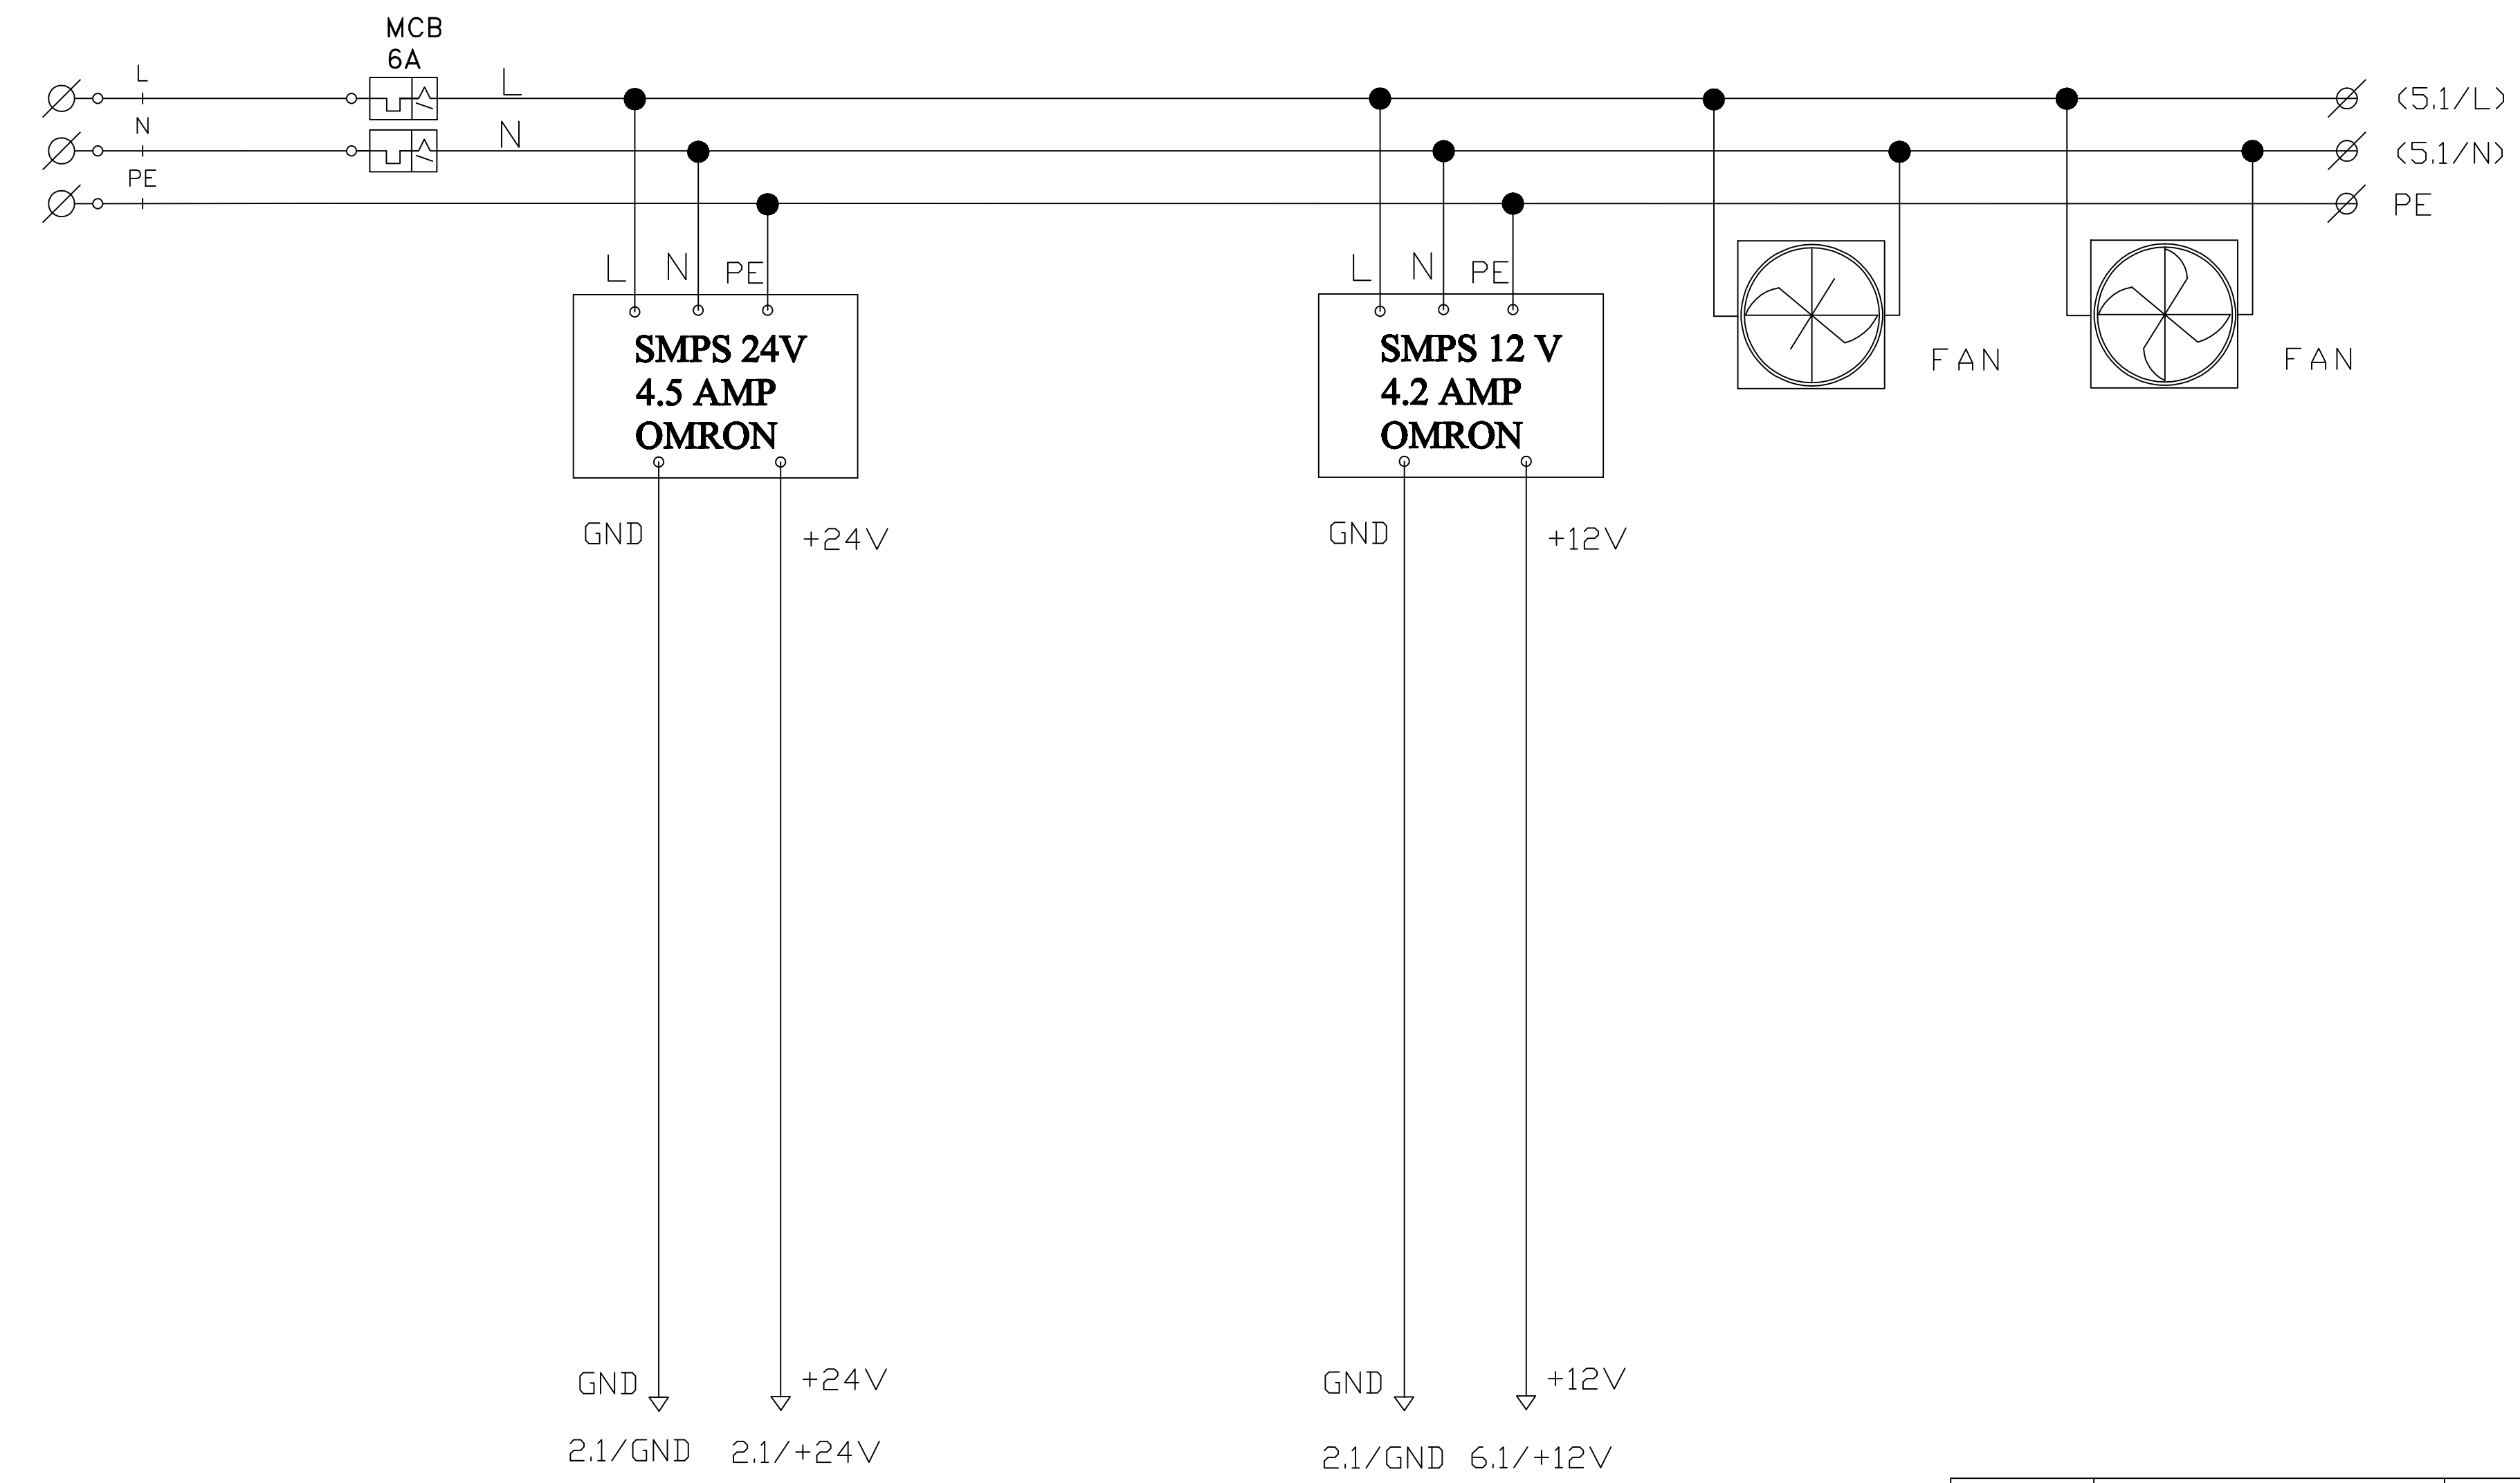


(5.1/L)
(5.1/N)
PE

FAN

FAN

TITLE :-
CONTROL DIAGRAM

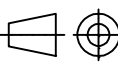18.05.2016	ISSUED FOR CLIENTS APPROVAL.	DARSHAN	CHITAMANI	
DATE	CHANGES	DRAWN	CHECKED	APPROVED
CLIENT:- MAGNETI MARELLI		 KONEM SOLUTIONS PIMPRI (PUNE)		
PROJECT :- END OF LINE TESTING AIM				PROJECTION 
SCALE : -NTS	QTY.:- 01 NO.	SHEET: 01 of 05	DRG NO :-	REV:- 1

A

B


C

D

E



F


12345678

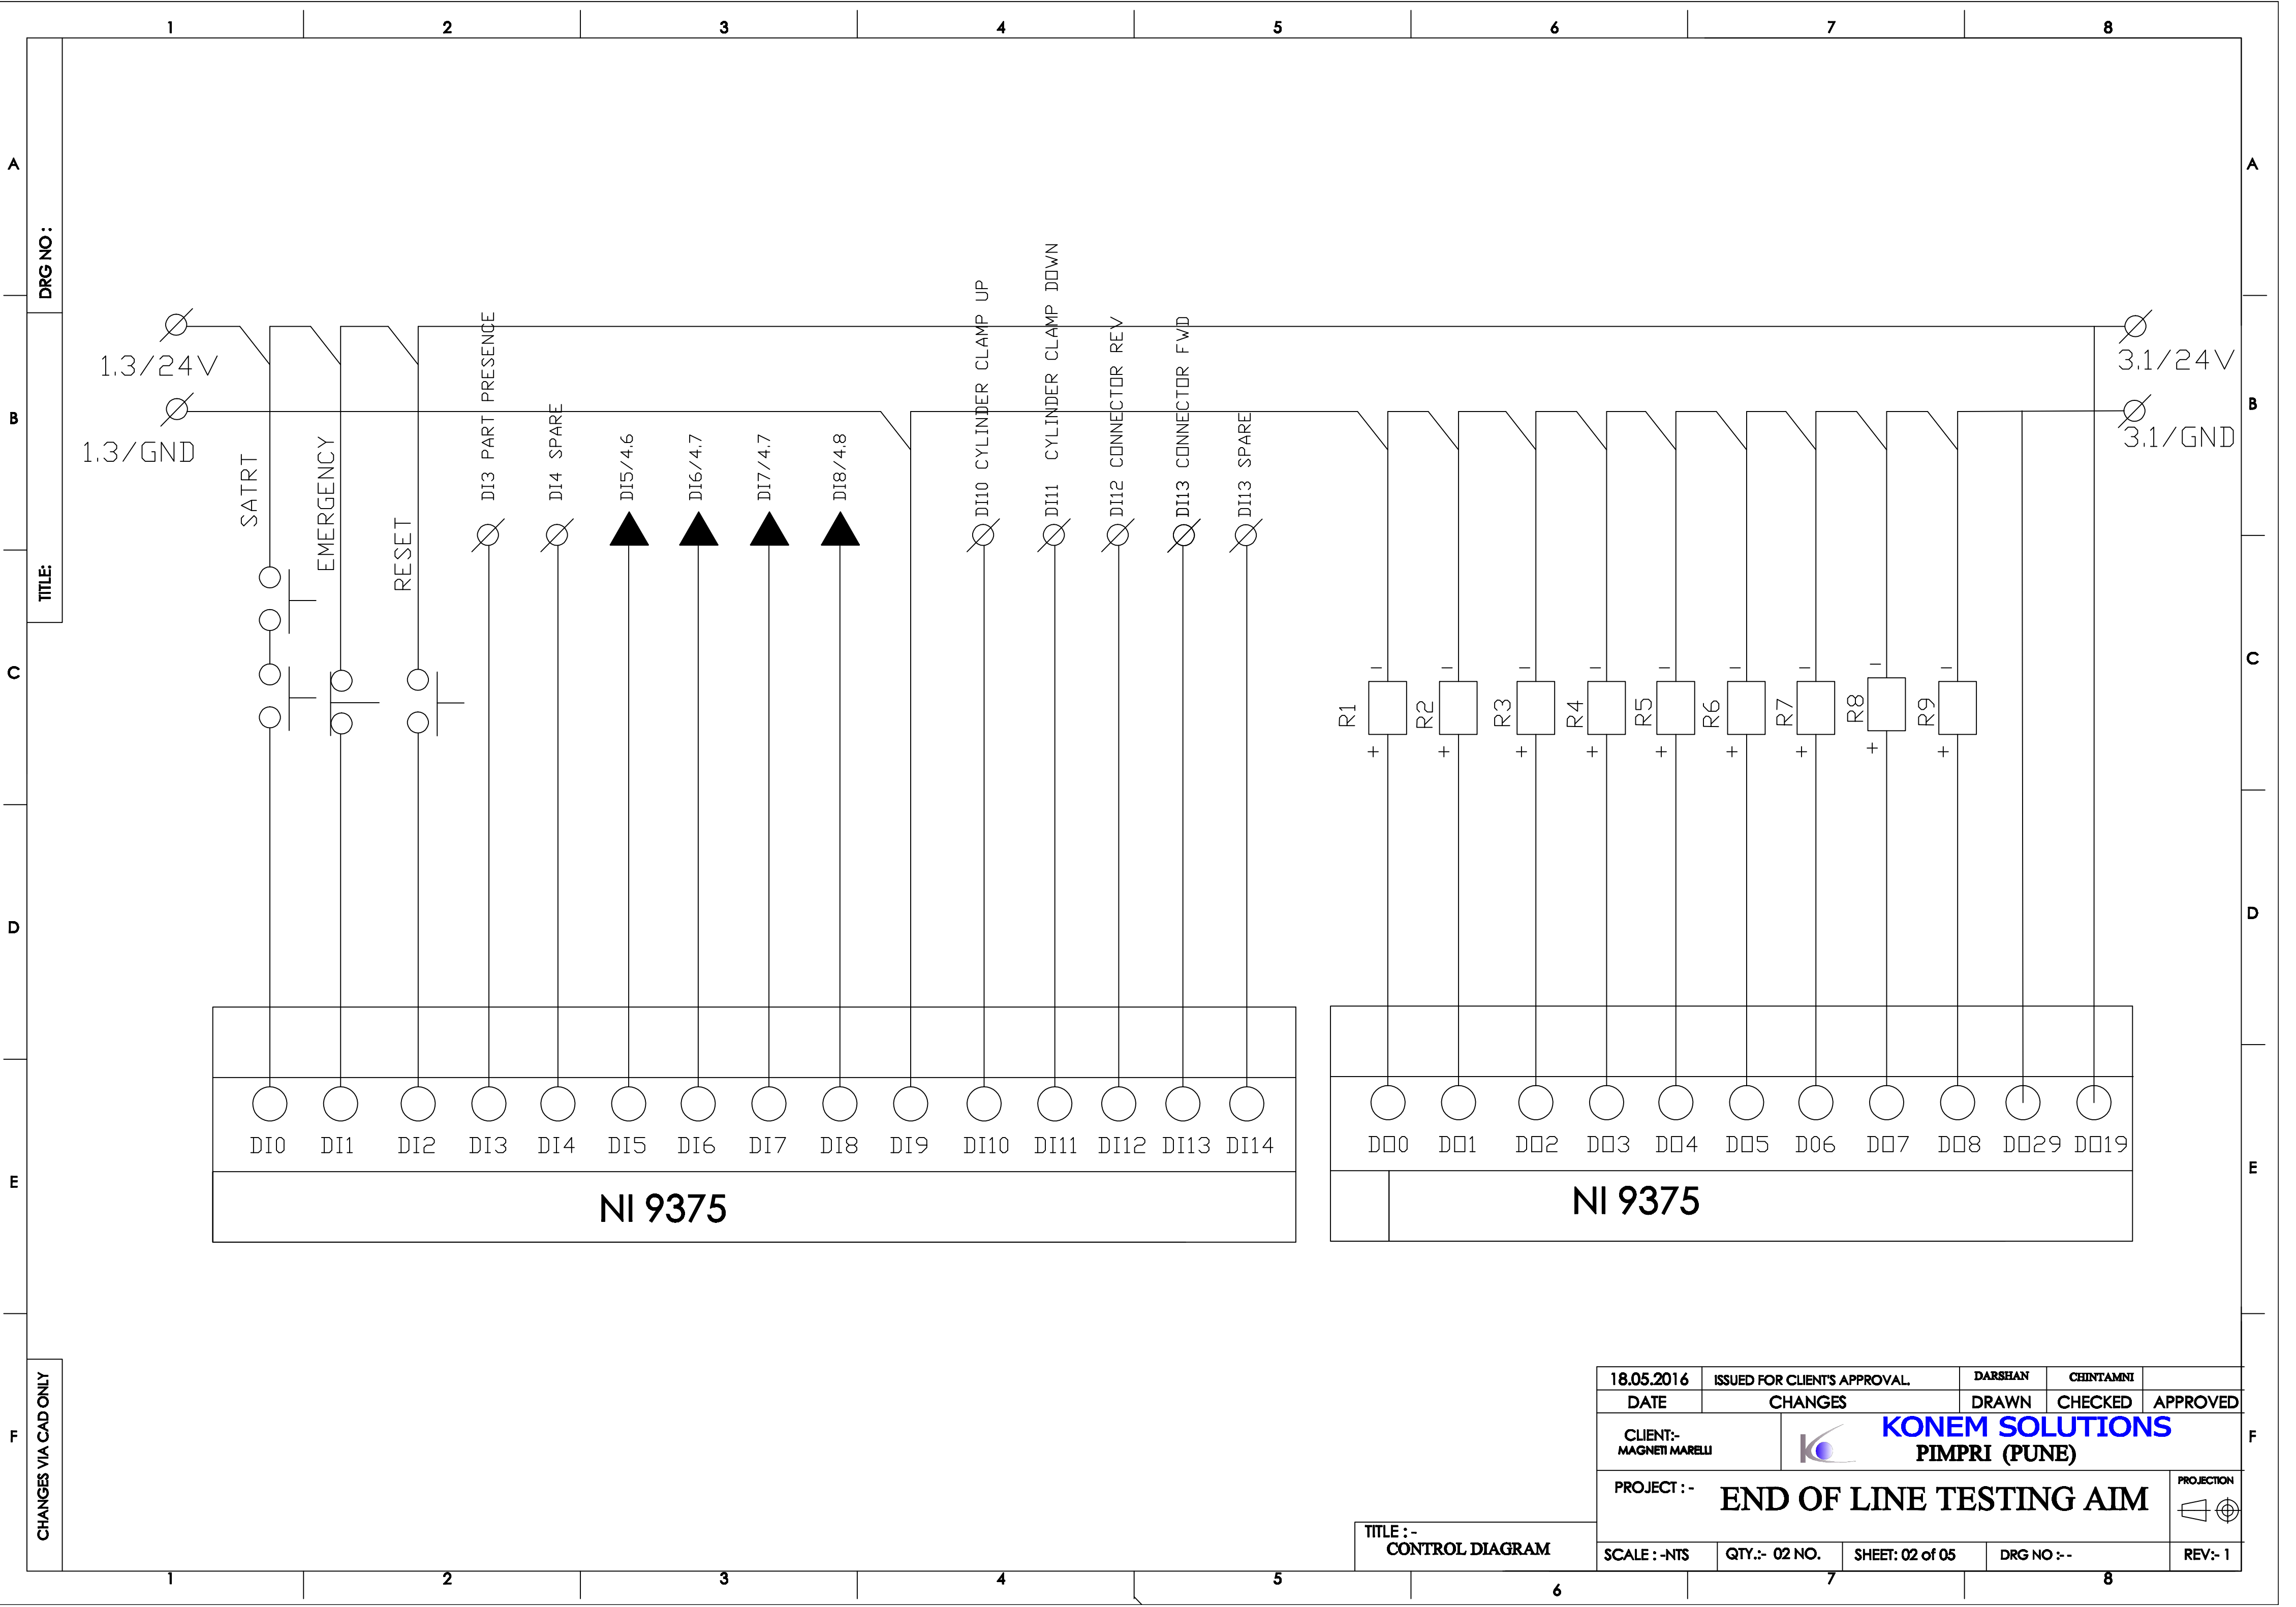


CHANGES VIA CAD ONLY

TITLE :-
CONTROL DIAGRAM

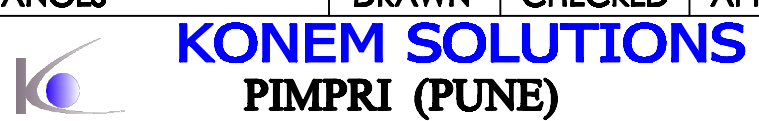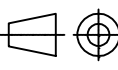
18.05.2016	ISSUED FOR CLIENT'S APPROVAL.	DARSHAN	CHINTAMNI	
DATE	CHANGES	DRAWN	CHECKED	APPROVED
CLIENT:- MAGNETI MARELLI				
PROJECT :- END OF LINE TESTING AIM				PROJECTION 
SCALE : -NTS	QTY.:- 02 NO.	SHEET: 02 of 05	DRG NO :-	REV:- 1

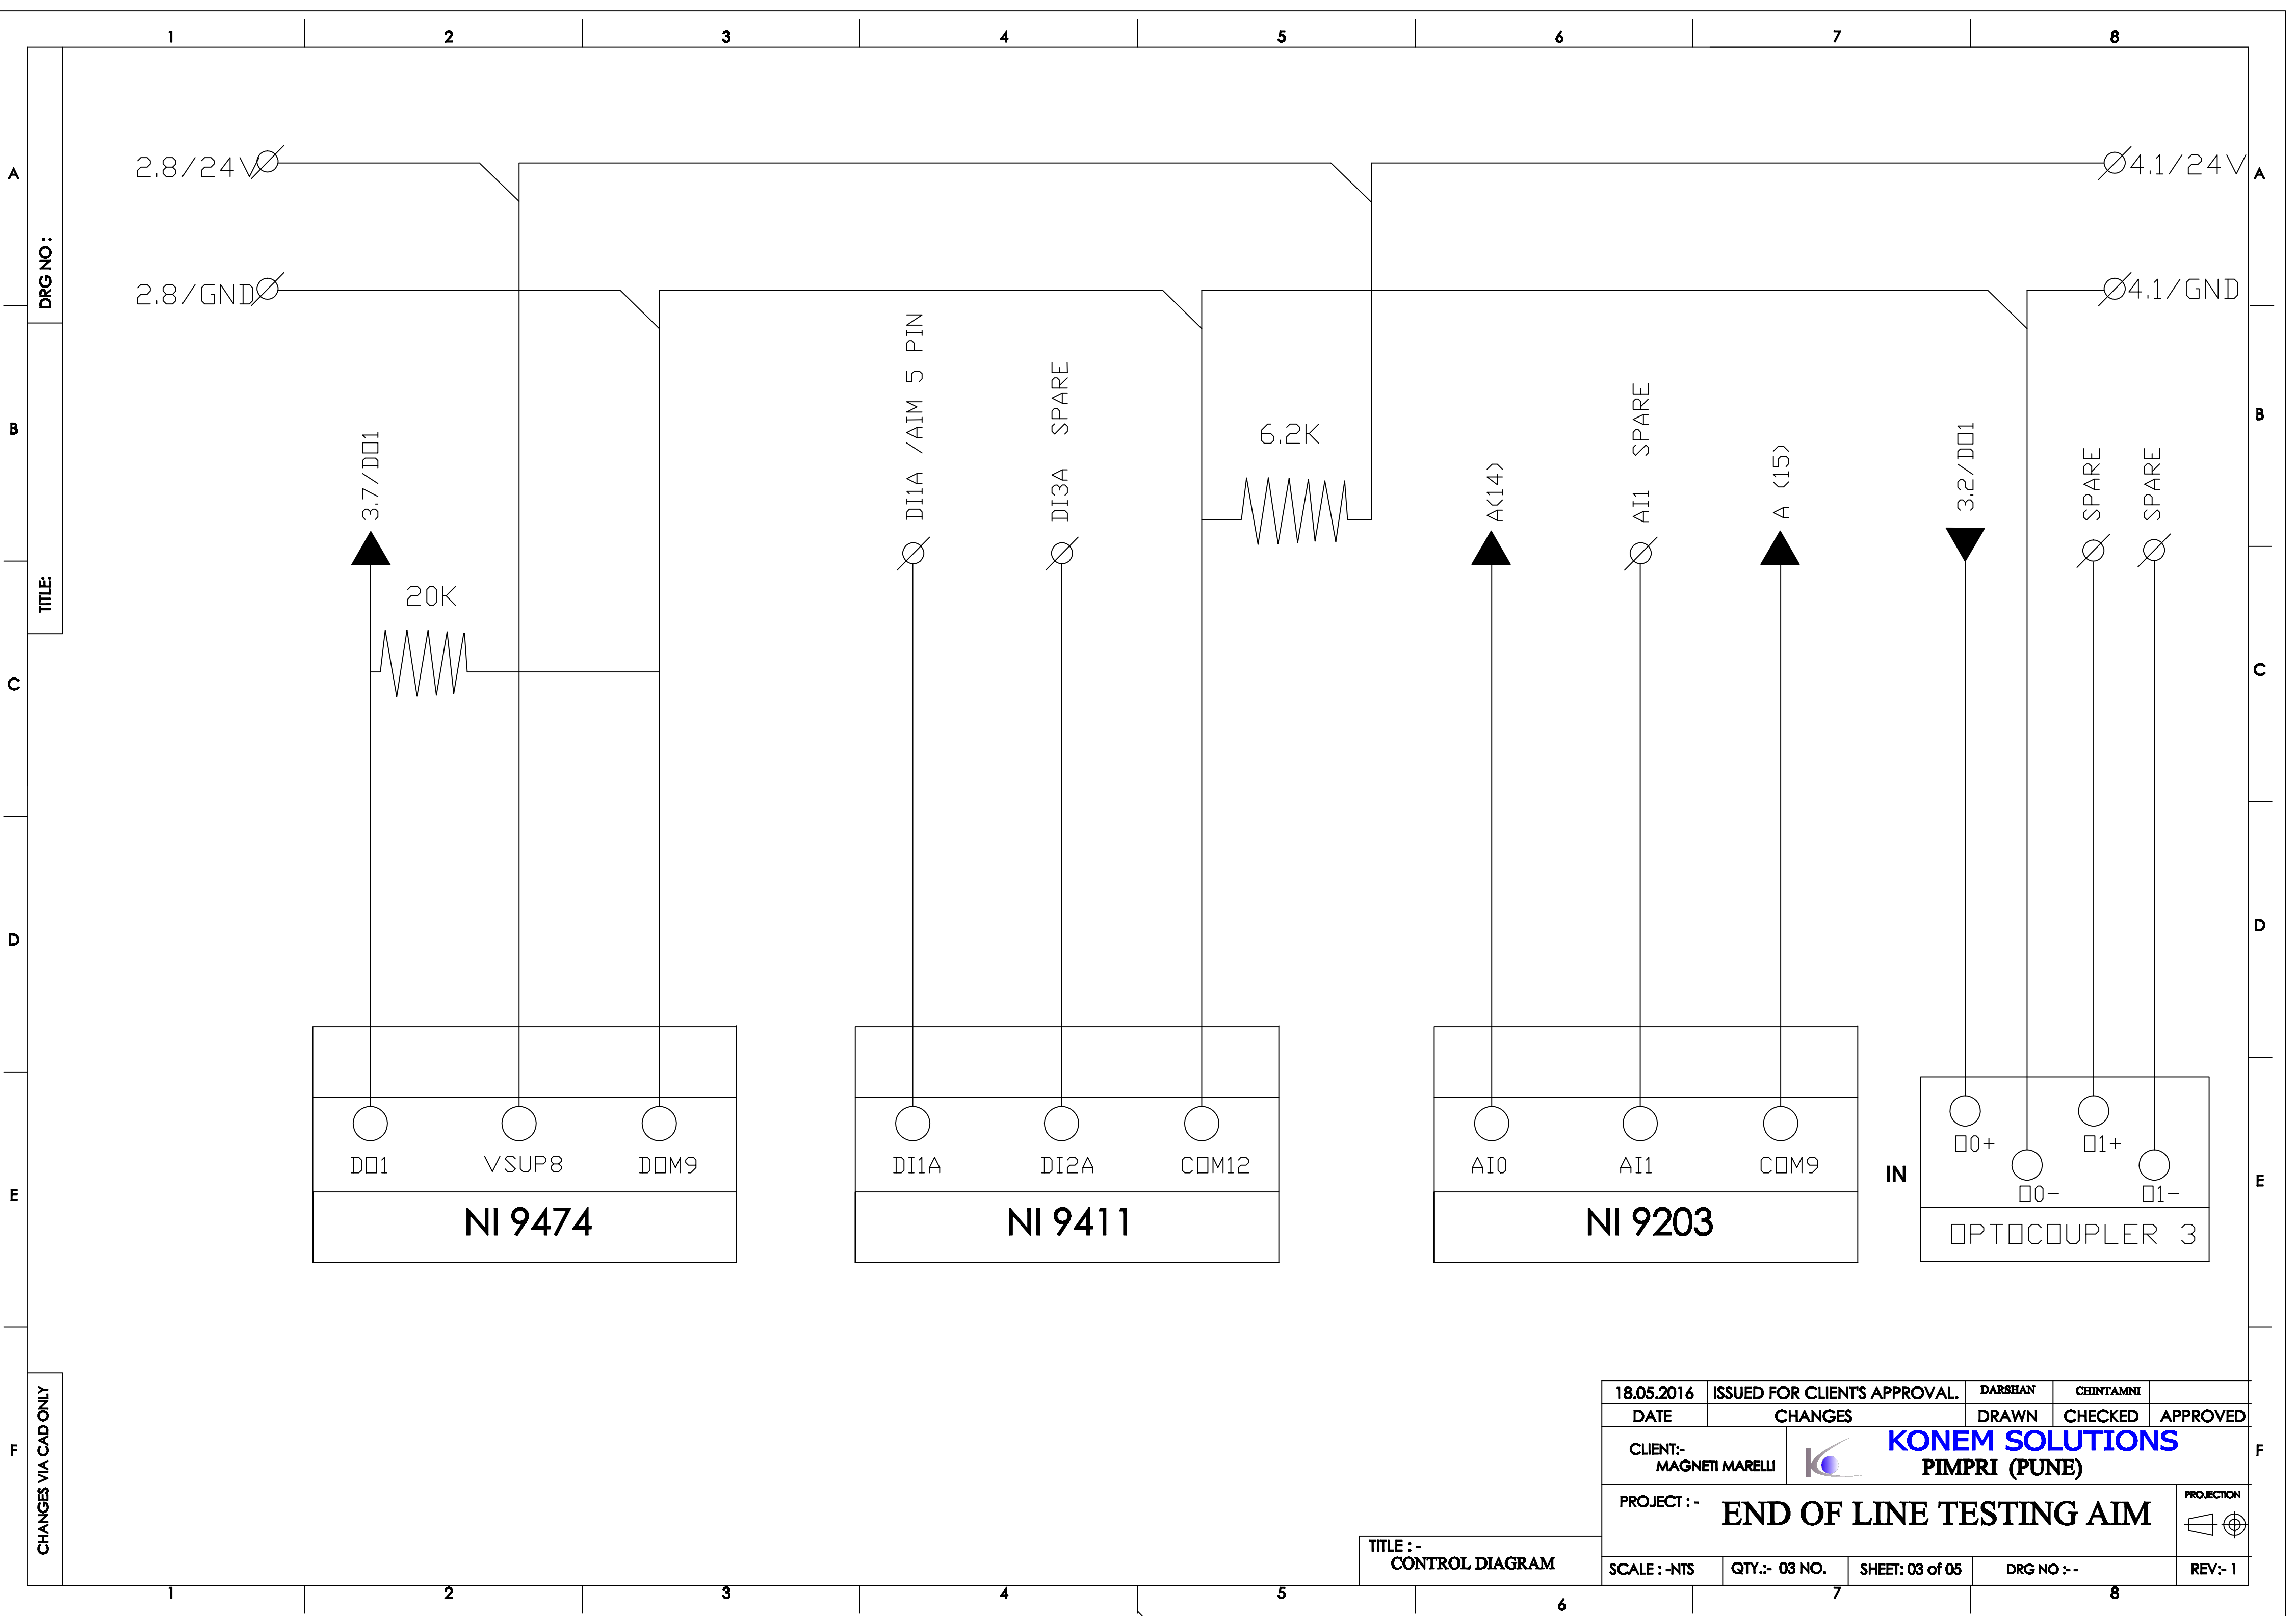


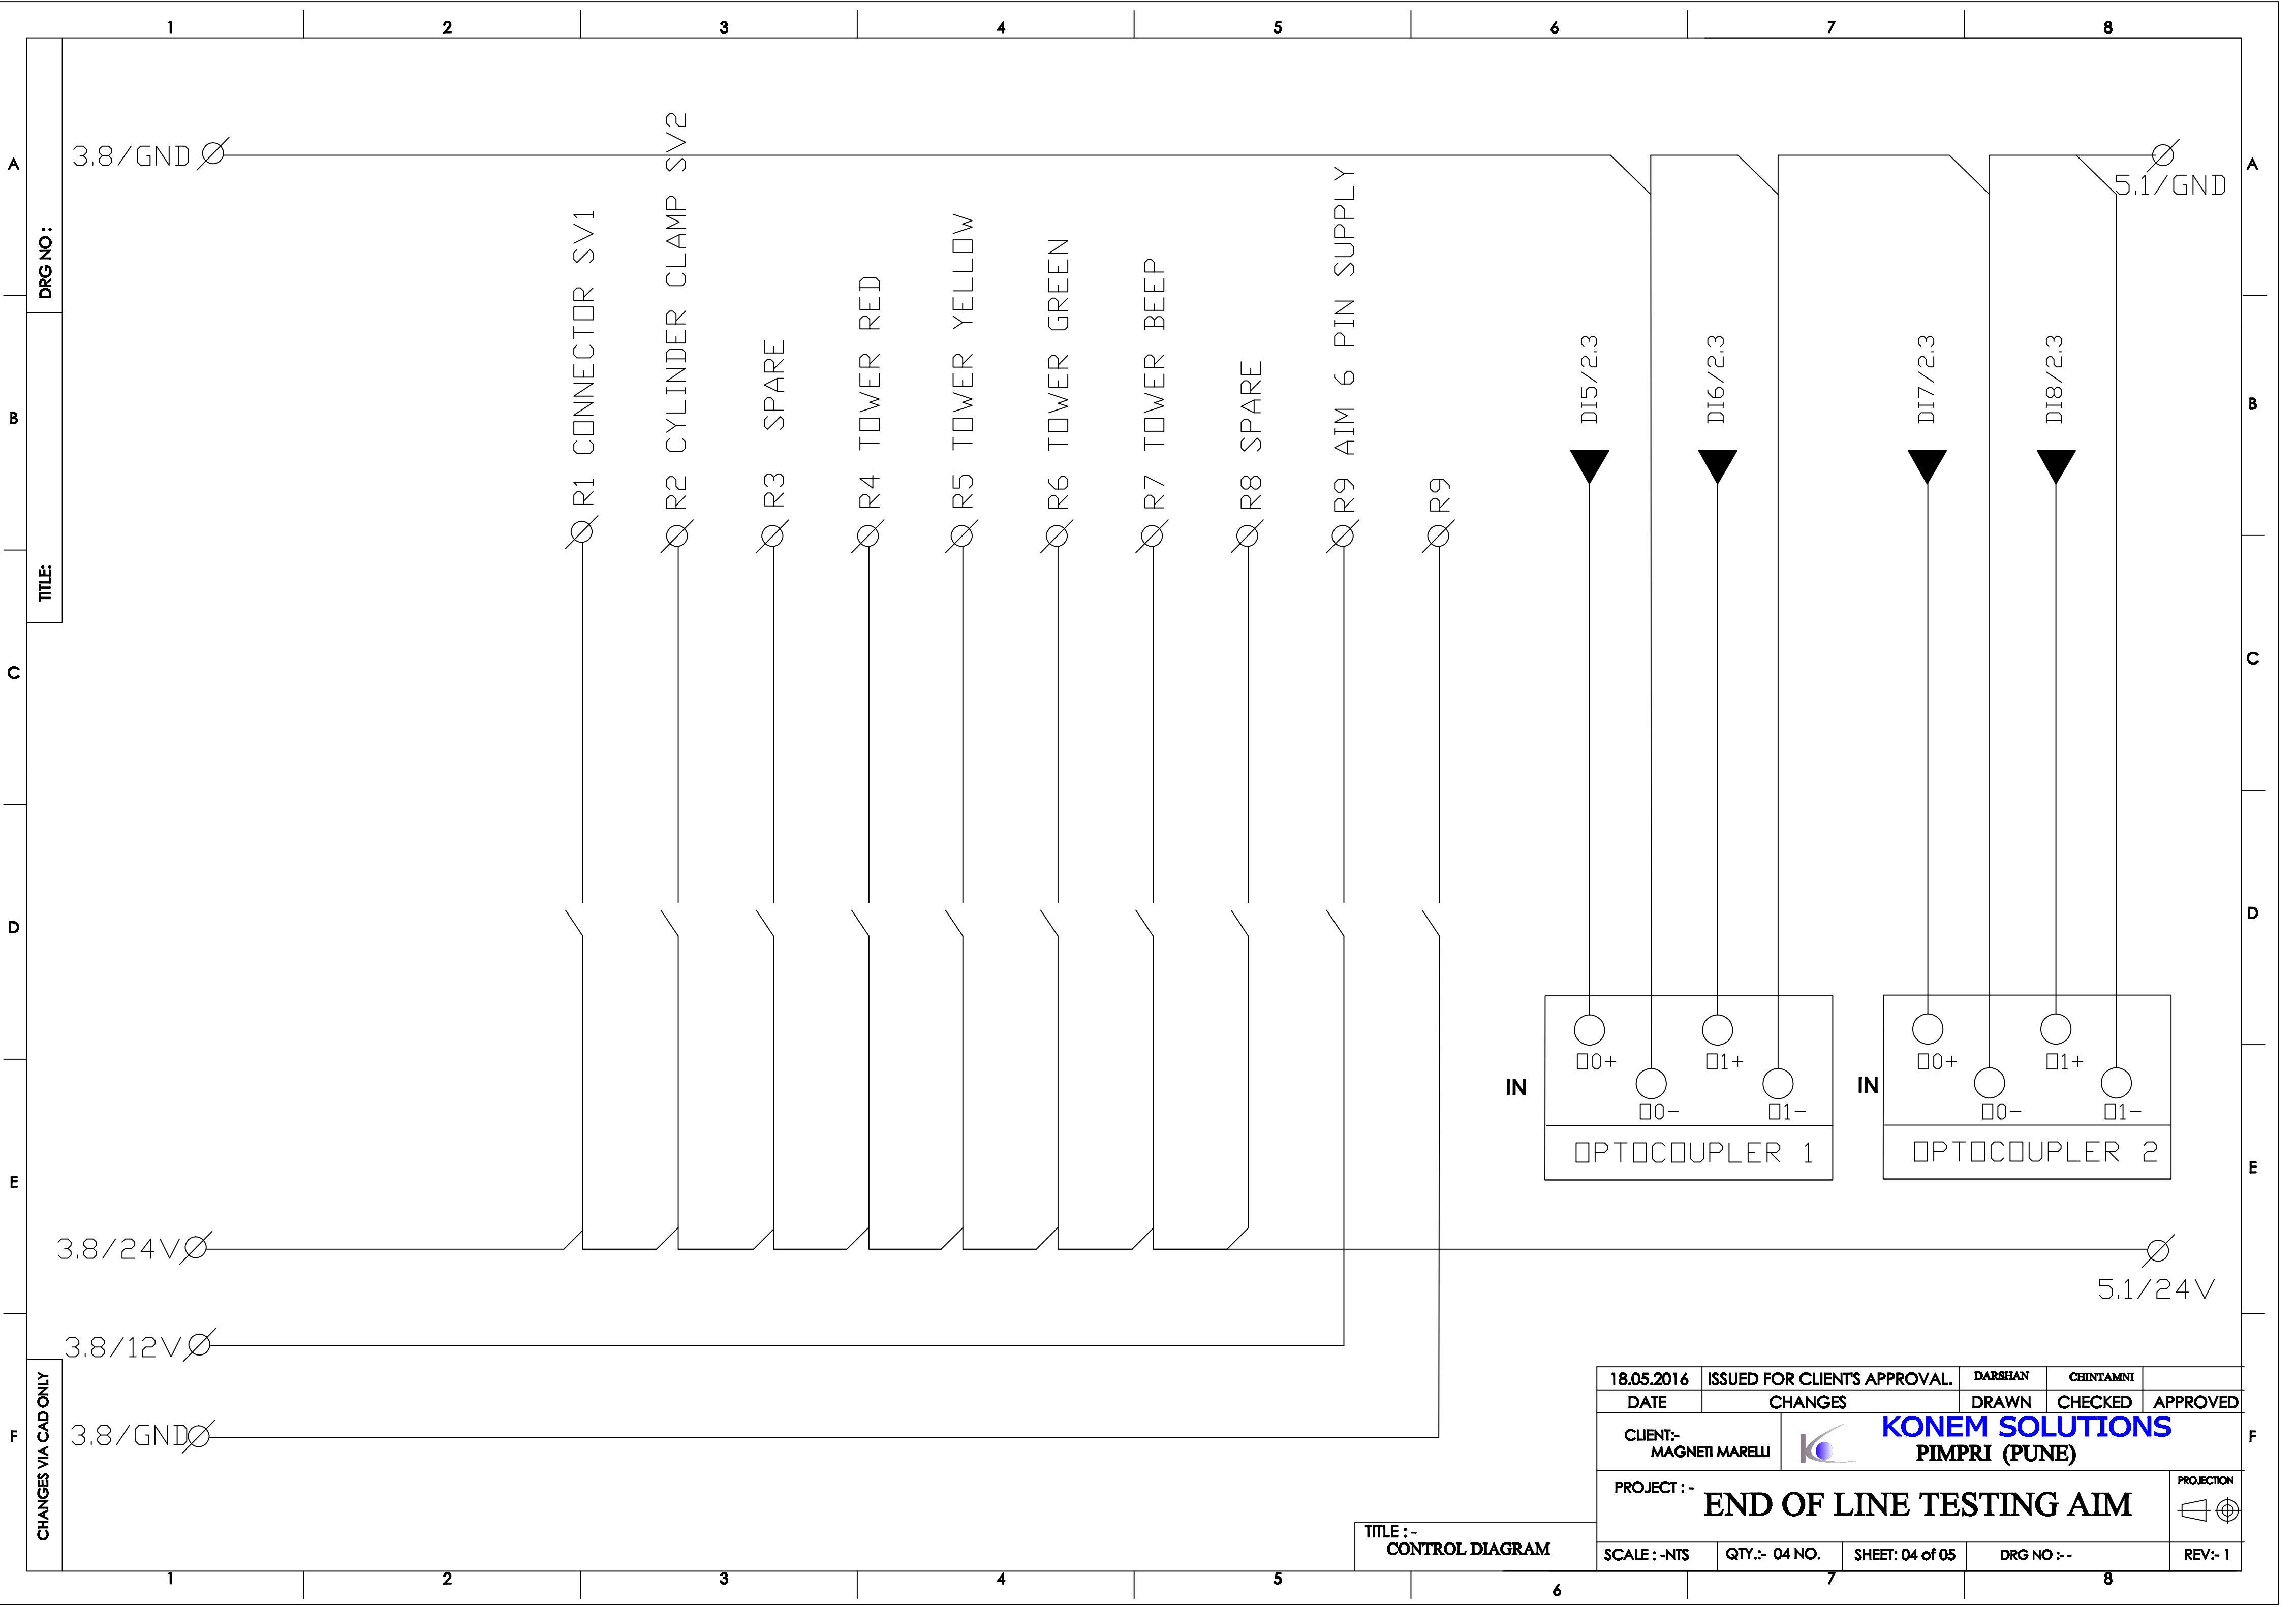

CHANGES VIA CAD ONLY

TITLE :-
CONTROL DIAGRAM

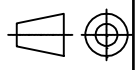
18.05.2016	ISSUED FOR CLIENT'S APPROVAL.	DARSHAN	CHINTAMNI	
DATE	CHANGES	DRAWN	CHECKED	APPROVED
CLIENT:- MAGNETI MARELLI				
PROJECT : - END OF LINE TESTING AIM				PROJECTION 
SCALE : -NTS	QTY.:- 04 NO.	SHEET: 04 of 05	DRG NO :-	REV:- 1

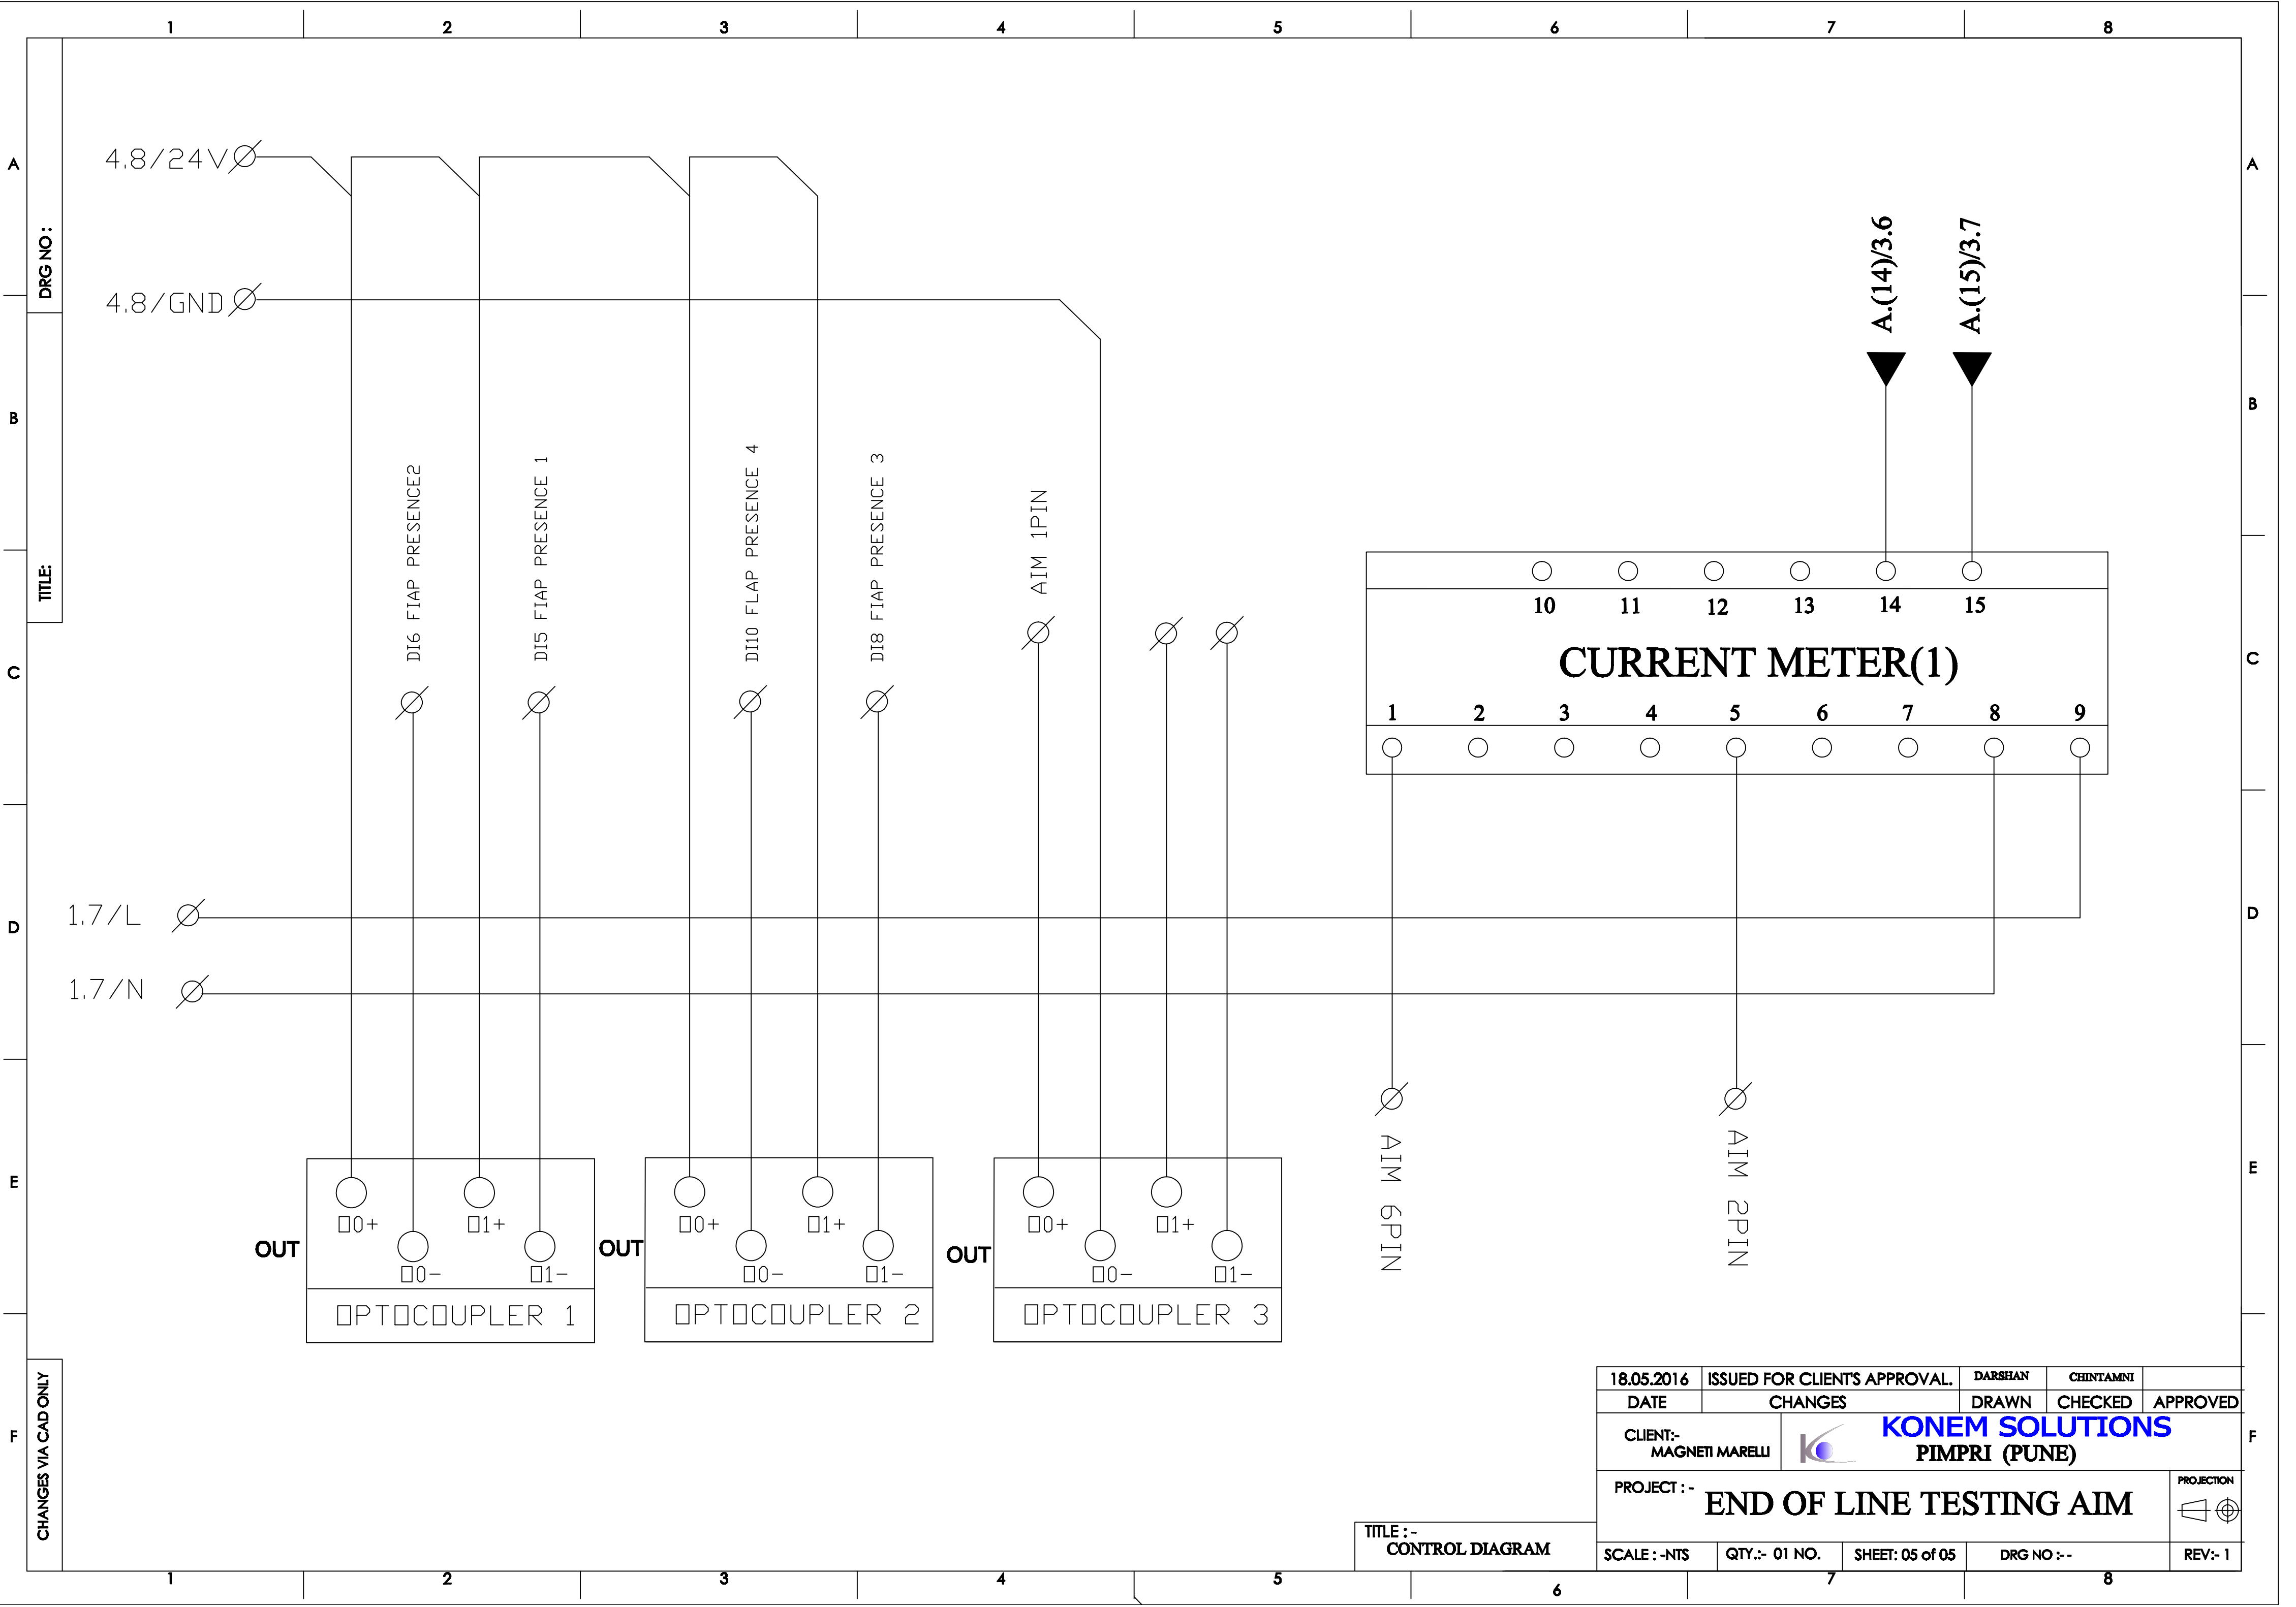

DRG NO.:

TITLE:

CHANGES VIA CAD ONLY

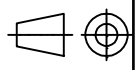18.05.2016	ISSUED FOR CLIENT'S APPROVAL.	DARSHAN	CHINTAMNI	
DATE	CHANGES	DRAWN	CHECKED	APPROVED
CLIENT:- MAGNETI MARELLI				
PROJECT : - END OF LINE TESTING AIM				PROJECTION 
SCALE : -NTS	QTY.:- 01 NO.	SHEET: 05 of 05	DRG NO :-	REV:- 1

TITLE :-
CONTROL DIAGRAM